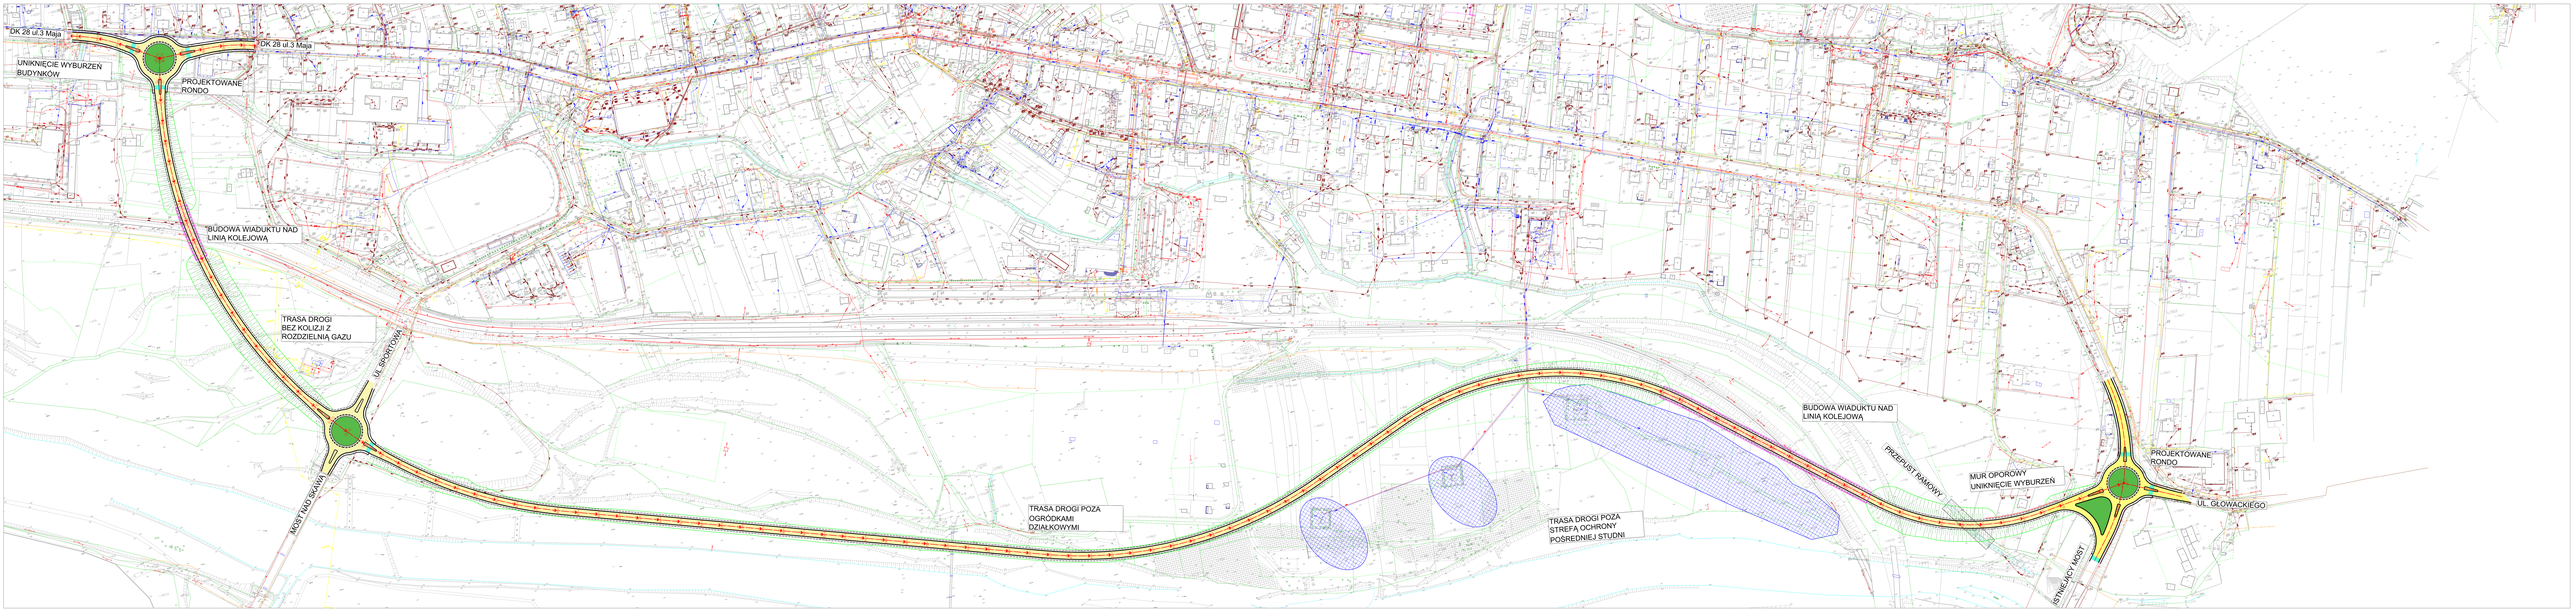
DK 28 ul.3 Maja
DK 28 ul.3 Maja
UNIKNIĘCIE WYBURZEŃ BUDYNKÓW
PROJEKTOWANE RONDO
BUDOWA WIADUKTU NAD LINIĄ KOLEJOWĄ
TRASA DROGI BEZ KOLIZJI Z ROZDZIELNIĄ GAZU
UL. SPORTOWA
MOST NAD SKAWĄ
TRASA DROGI POZA OGRODKAMI DZIAŁKOWYMI
TRASA DROGI POZA STREFĄ OCHRONY POŚREDNIEJ STUDNI
BUDOWA WIADUKTU NAD LINIĄ KOLEJOWĄ
PRZEPUST RAMOWY
MUR OPOROWY UNIKNIĘCIE WYBURZEŃ
PROJEKTOWANE RONDO
UL. GŁOWACKIEGO
ISTNIEJĄCY MOST